
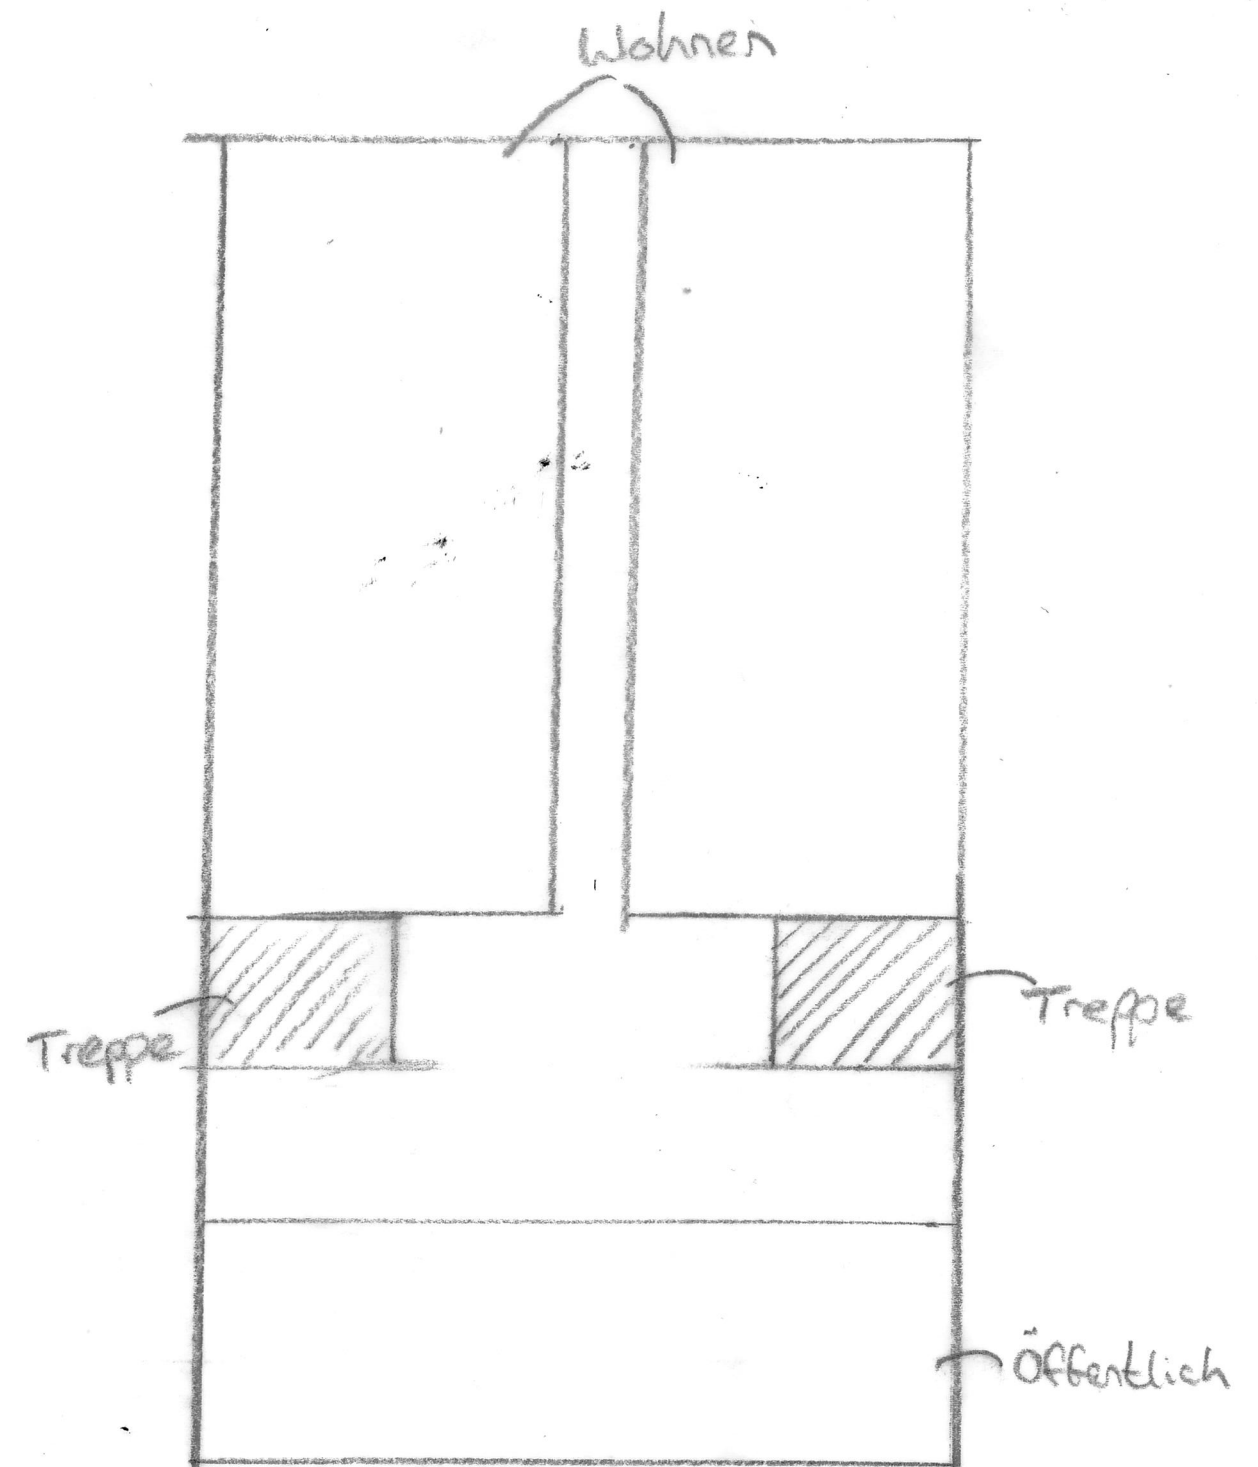


VOM STADTEBAU ZUR ARCHITEKTUR

Übung 3


SAG 2

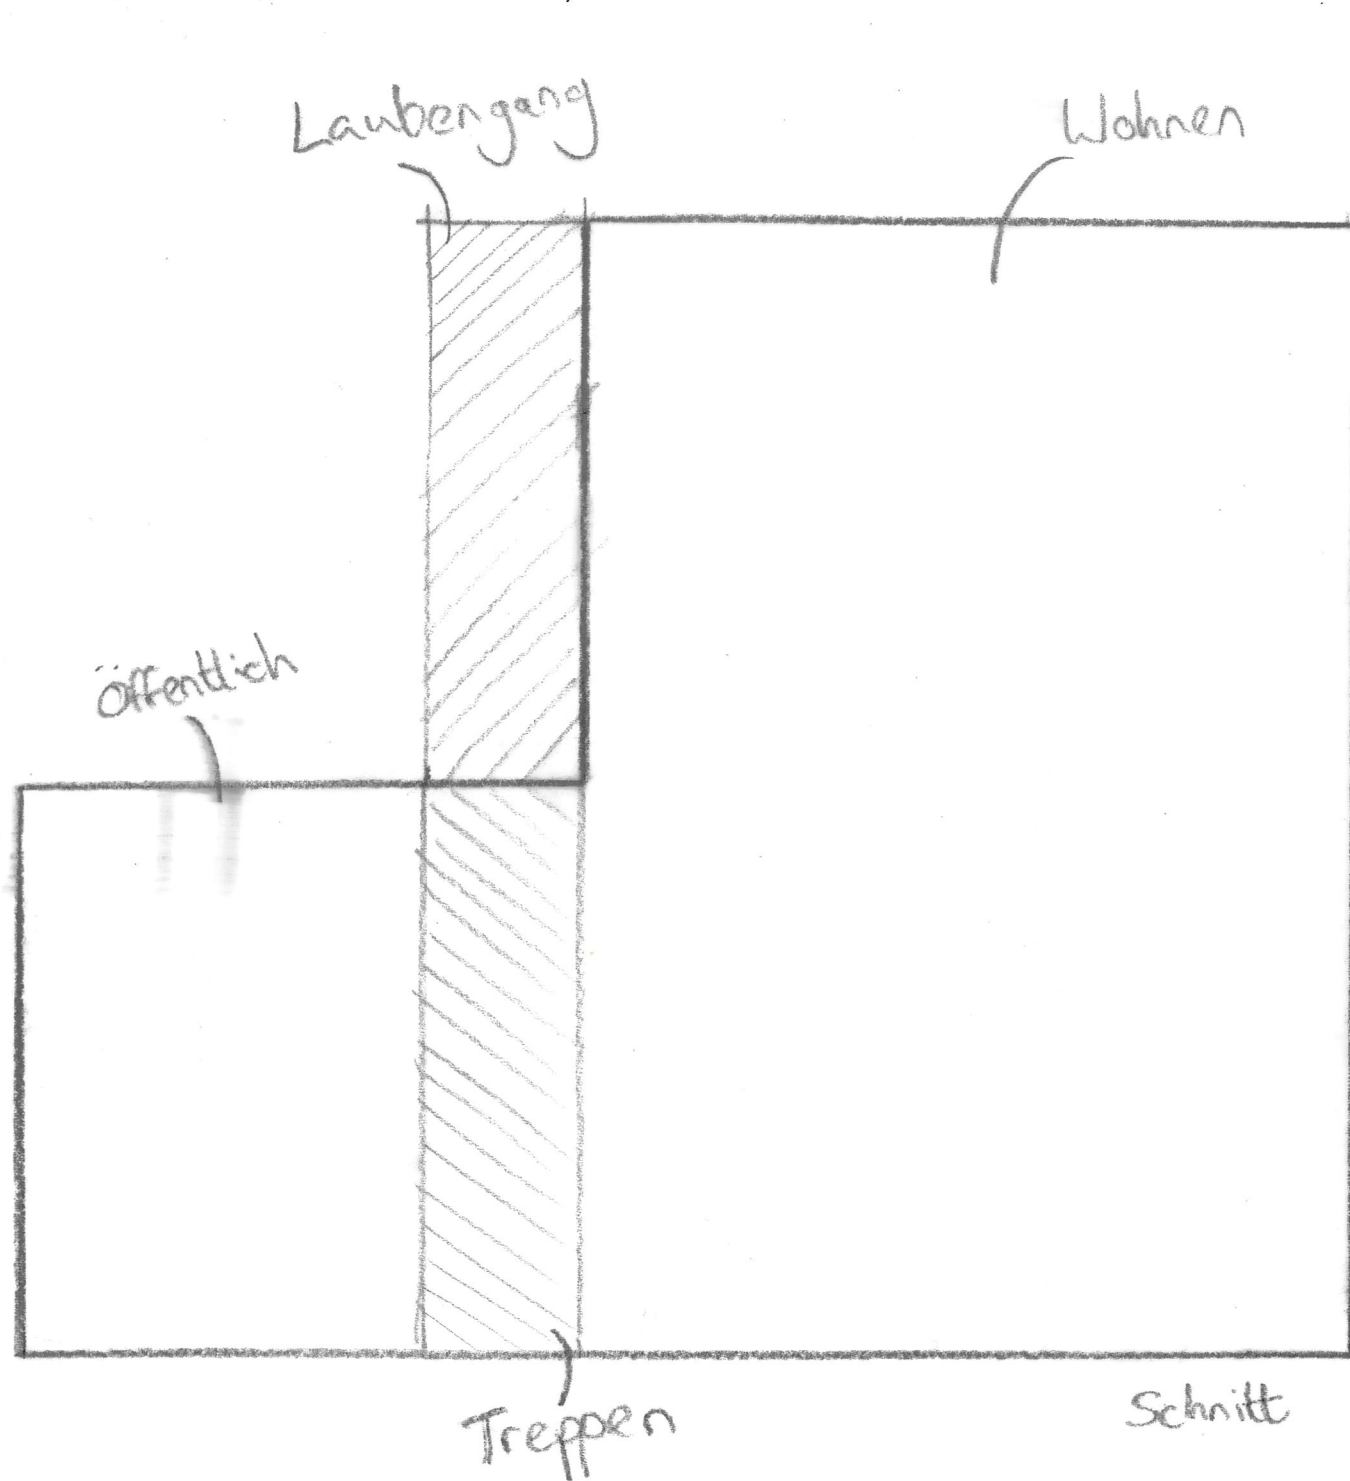

VOM VOLUMEN ZUM WOHNEN

Übung 4

SAG 2

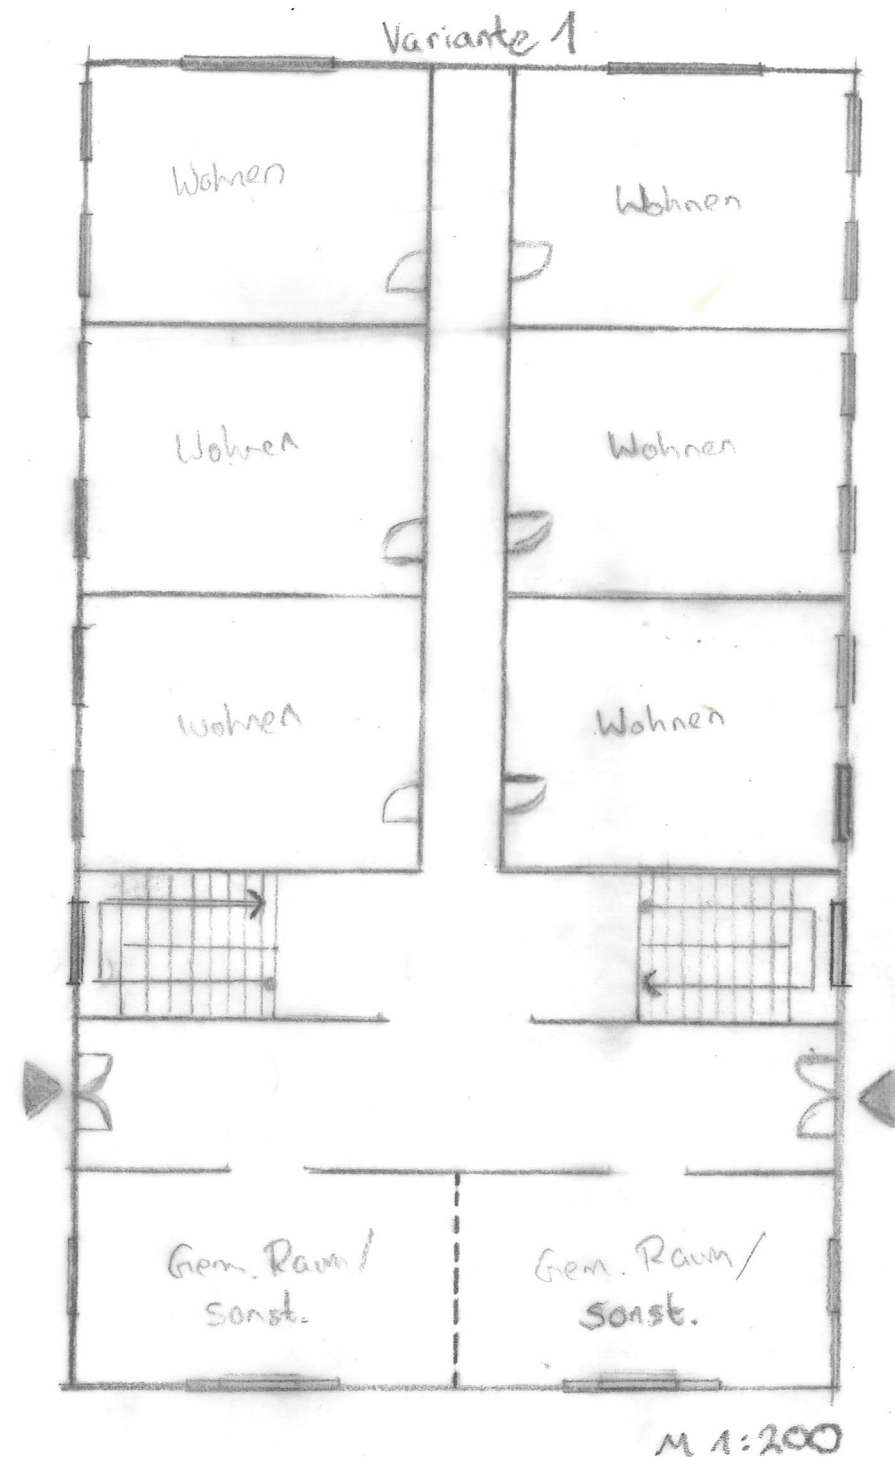


Variante 1:

Der EG-Grundriss verbindet Wohnen mit öffentlich nutzbaren Gemeinschaftsräumen. Die vertikale Erschliessung erfolgt durch U-förmige Treppen, mit Zwischenpodest auf beiden Seiten, für Symmetrie und die Möglichkeit den Grundriss im OG zu variieren.

Variante 2:


Der EG-Grundriss verbindet ebenso Wohnen mit öffentlich nutzbaren Gemeinschaftsräumen, lässt jedoch mehr Platz für sonstige Nutzungen, die kein Licht benötigen.

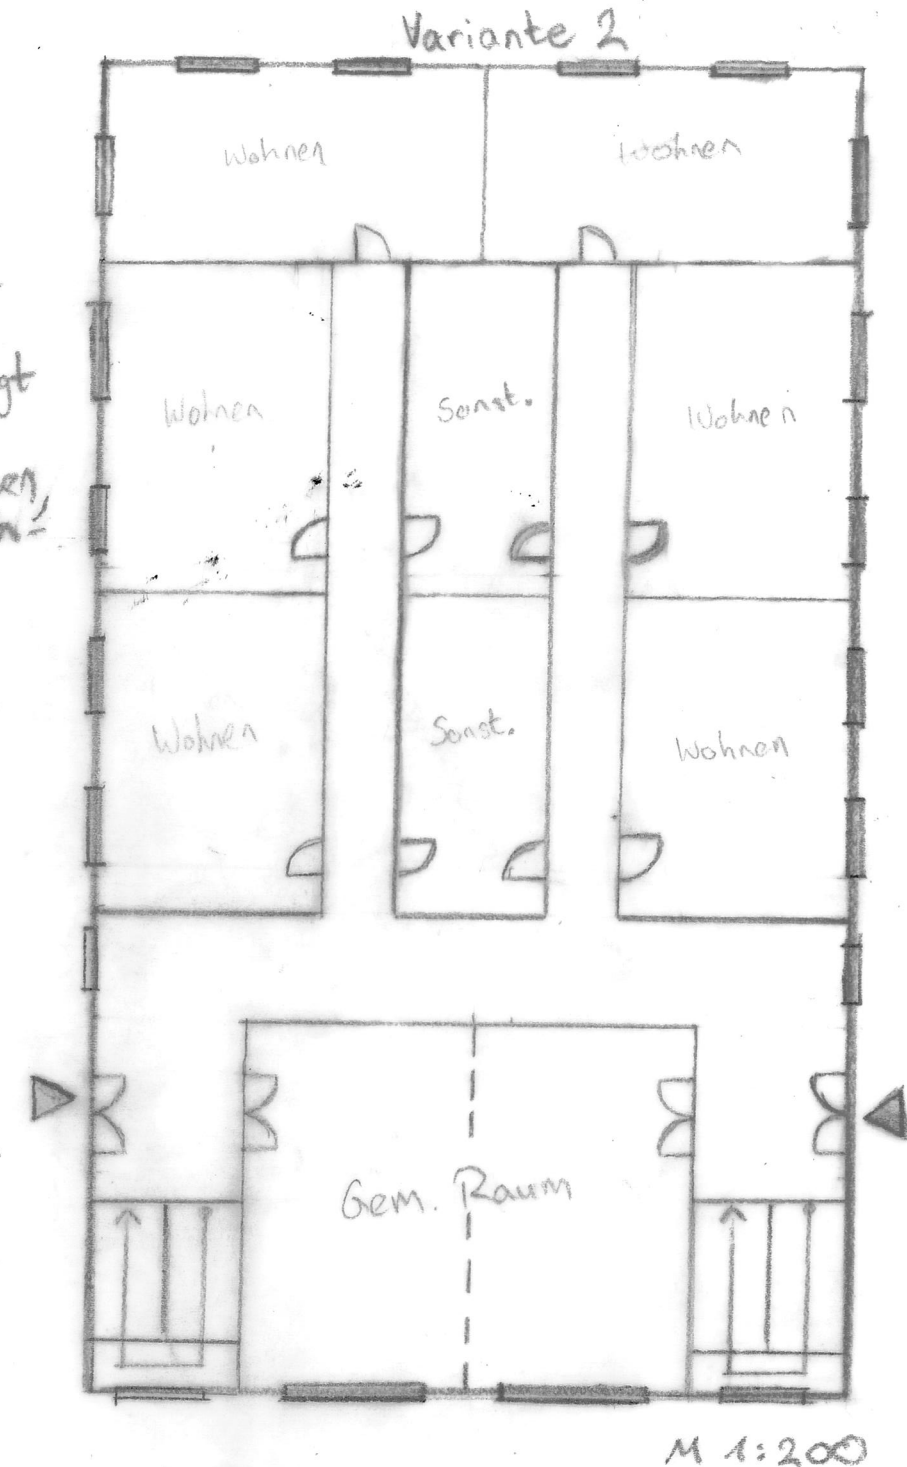

VOLUMENMODELL WIRD SCHICHTMODELL

Übung 5

SAG 2

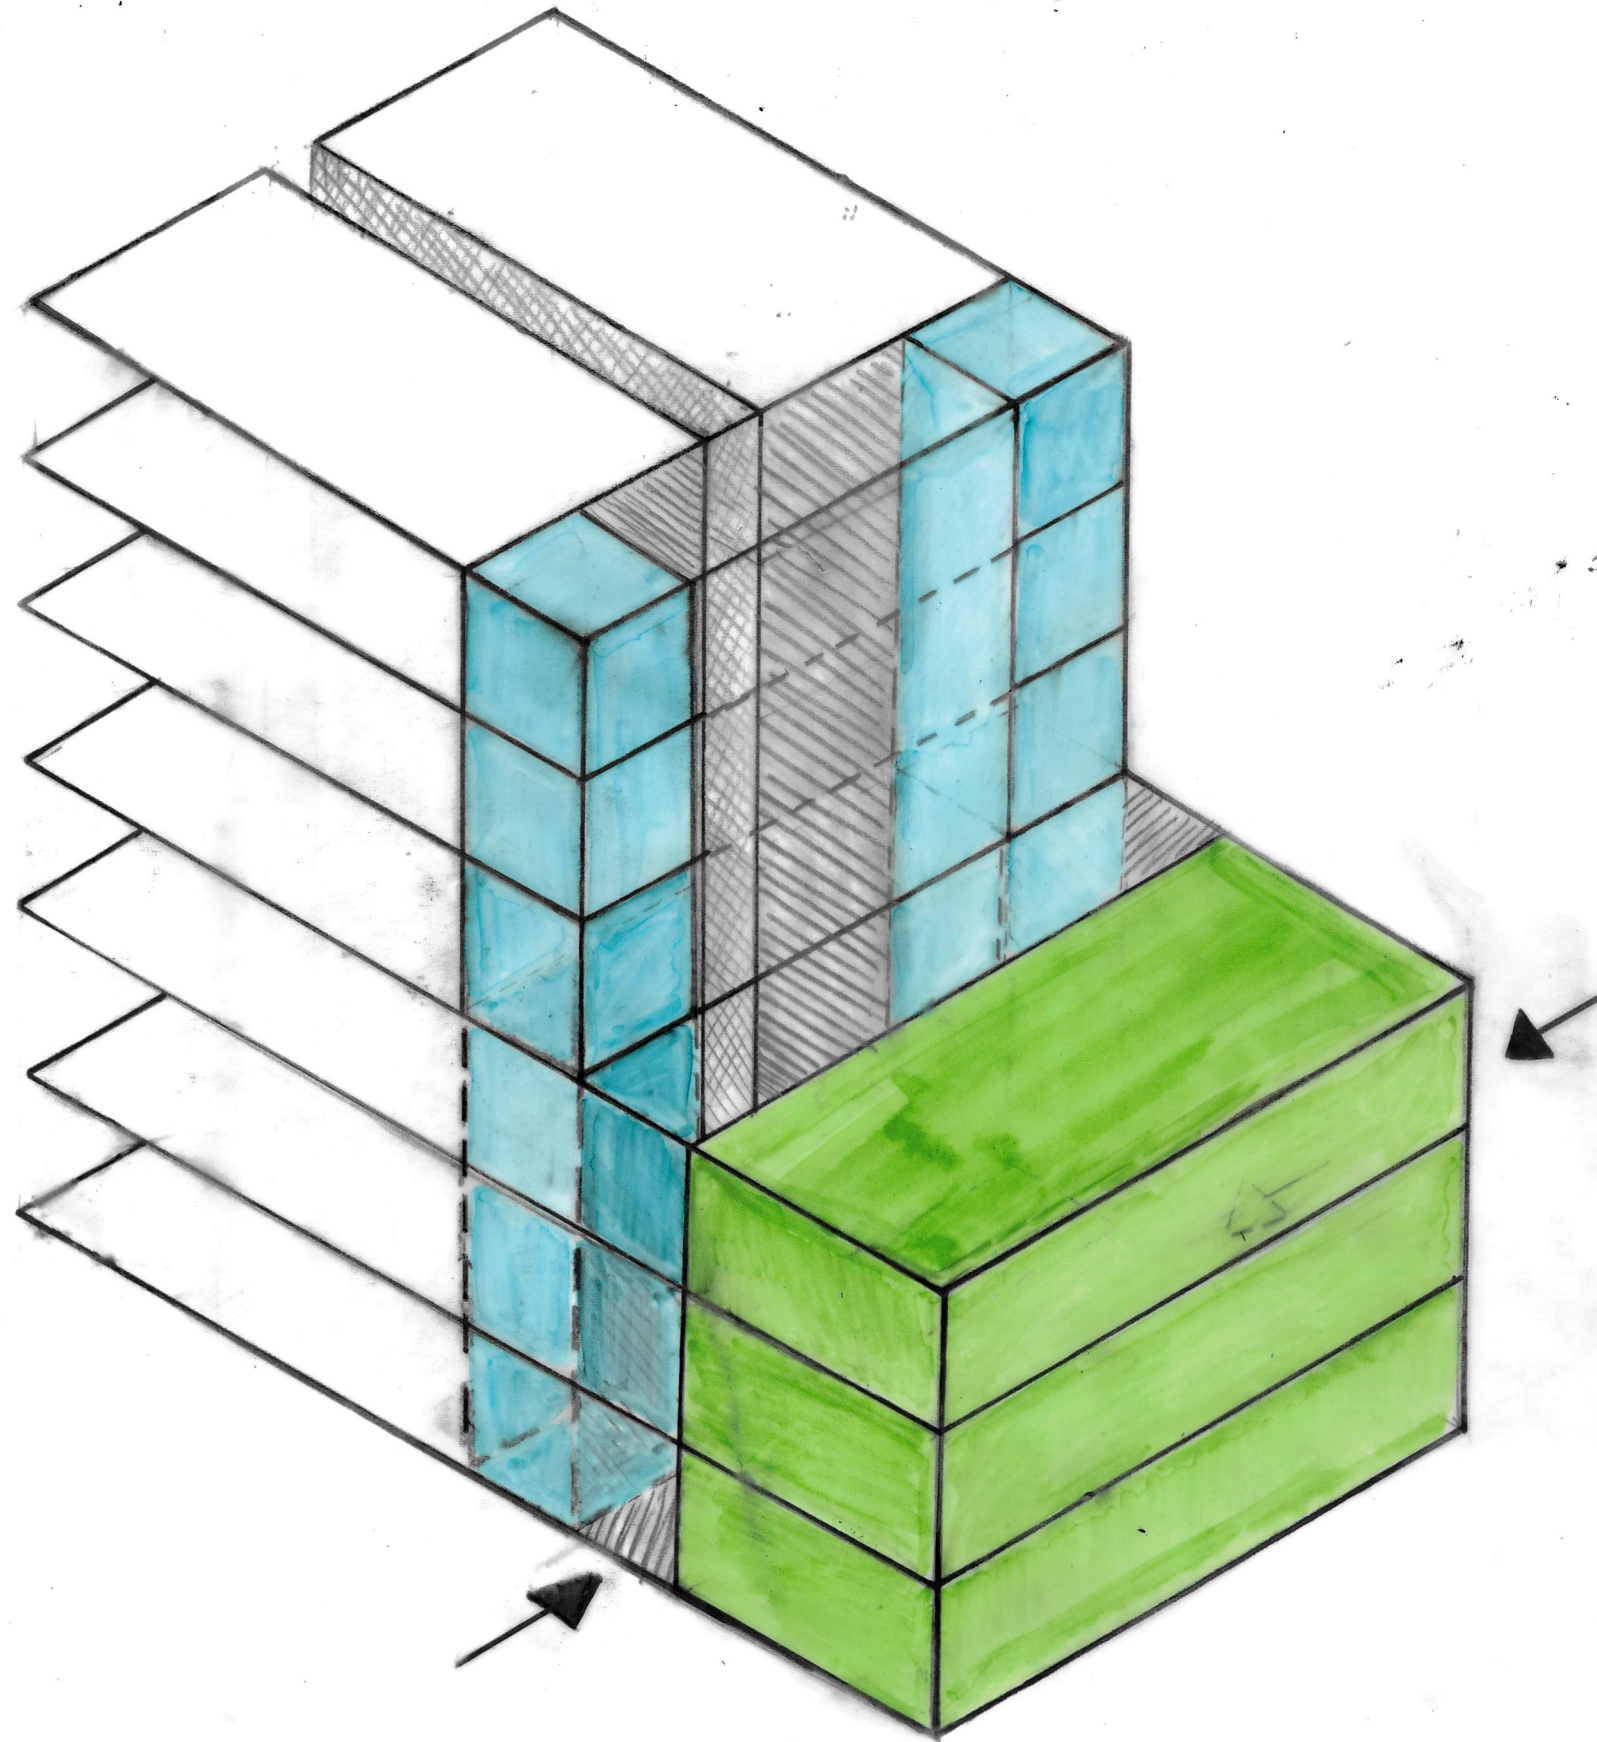


- Öffentlich
- Erschliessung
- Voids

David Runge 1498345

SCHNITTSTUDIEN

Übung 6

SAG 2

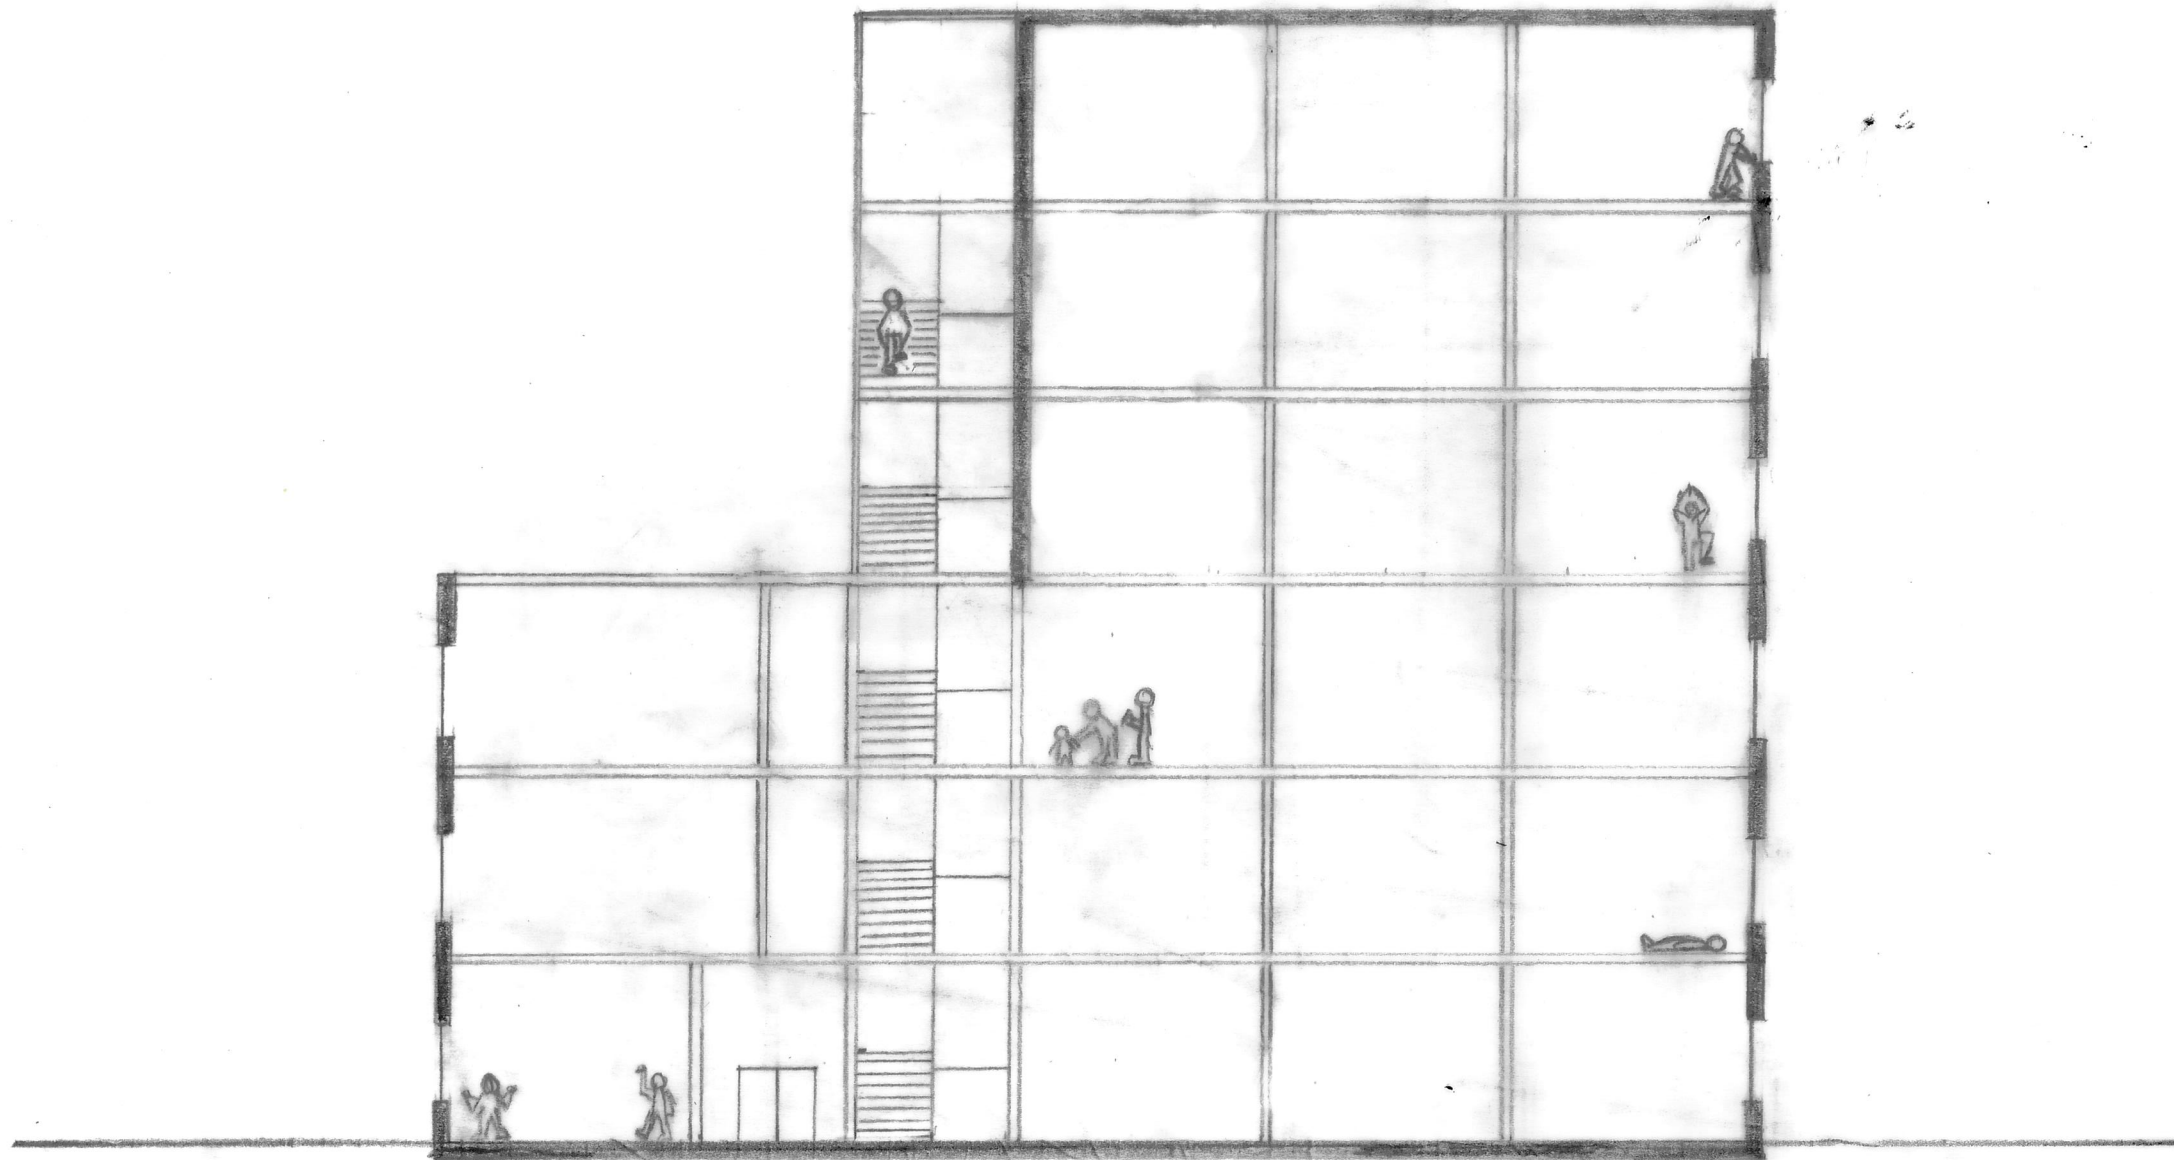

M 1:200

David Ringe 1498345

FASSADE LESEN

Exkursionsübung 2


SAG 2

ZURÜCKHALTEND

RYTHMISCH

GESCHLOSSEN

Durch den gleichmäßigen
Wechsel aus Fenster, Loggia
und Wand wirkt die Fassade
ordnend auf den Stadtraum

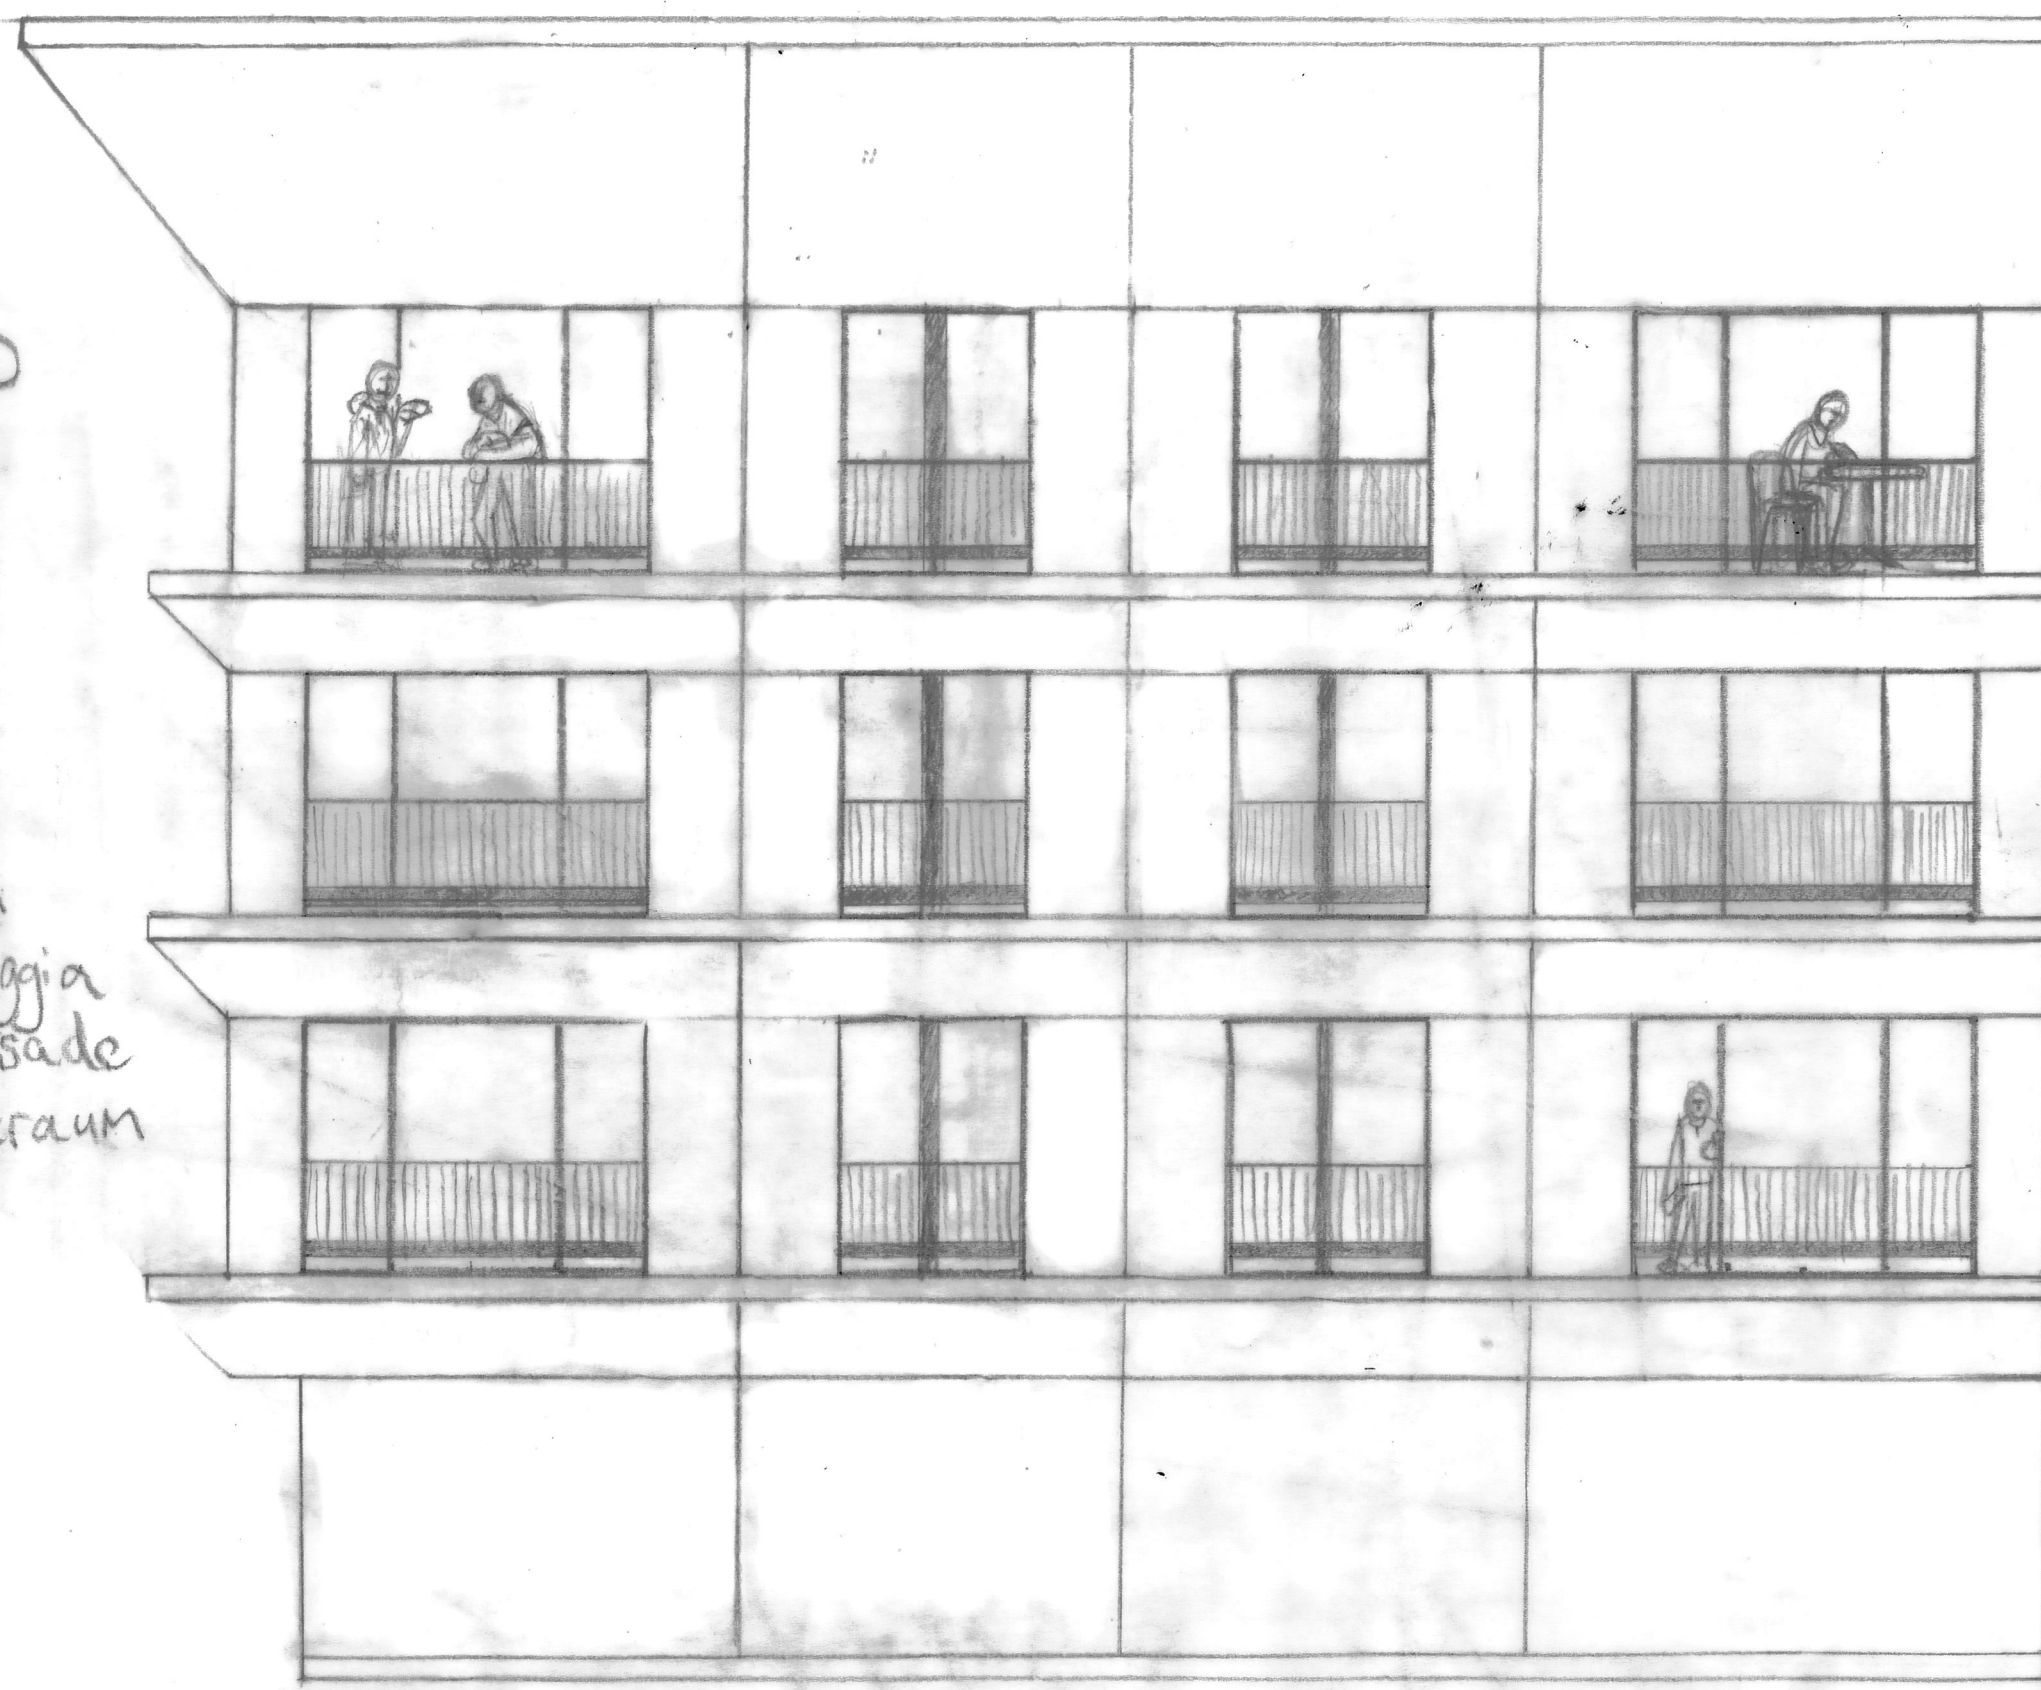

David Ringe 1498345